

TAB 16



Board of Education Report

[Back to Order of Business](#)

File #: 025-22/23, **Version:** 1

Resolution of Intention to Dedicate Easements to the County of Los Angeles at Wisdom Elementary School

PROJECT NAME: 73RD STREET AND ALLEYS
EAST OF CENTRAL AVENUE
73RD STREET (1-2RE)
A.M.B. 6024-001
I.M. 099-197
R.D. 241
S.D. 2
LV19000342

EXHIBIT “A”
LEGAL DESCRIPTION
STREET DEDICATION

PARCEL A, NO. 1-2RE: (EASEMENT FOR PUBLIC ROAD AND HIGHWAY PURPOSES)

THOSE PORTIONS OF LOTS 794 THROUGH 799, INCLUSIVE, IN THE UNINCORPORATED TERRITORY OF THE COUNTY OF LOS ANGELES, STATE OF CALIFORNIA, AS SHOWN ON TRACT NO. 5450, RECORDED IN BOOK 59, PAGES 94 AND 95 OF MAPS, IN THE OFFICE OF THE RECORDER FOR SAID COUNTY, DESCRIBED AS FOLLOWS:

COMMENCING AT THE CENTERLINE INTERSECTION OF FLORENCE AVENUE AND CENTRAL AVENUE (EACH 100.00 FEET WIDE); THENCE ALONG SAID CENTERLINE OF CENTRAL AVENUE, SOUTH 00°03'28" WEST, 50.00 FEET TO THE WESTERLY PROLONGATION OF THE SOUTHERLY RIGHT OF WAY LINE OF FLORENCE AVENUE; THENCE ALONG SAID WESTERLY PROLONGATION, SOUTH 89°44'28" EAST 77.10 FEET TO THE **TRUE POINT OF BEGINNING**, BEING THE EASTERLY TERMINUS OF A 27.00-FOOT RADIUS CURVE, CONCAVE SOUTHEASTERLY AND TANGENT AT SAID EASTERLY TERMINUS TO SAID SOUTHERLY RIGHT OF WAY LINE OF FLORENCE AVENUE, AND TANGENT AT ITS SOUTHERLY TERMINUS TO THE EASTERLY RIGHT OF WAY LINE OF CENTRAL AVENUE; THENCE THE FOLLOWING NUMBERED COURSES:

1. LEAVING SAID SOUTHERLY RIGHT OF WAY LINE OF FLORENCE AVENUE, SOUTH 51°30'14" WEST, 32.09 FEET TO A LINE PARALLEL WITH AND 52.00 FEET EASTERLY OF SAID CENTERLINE OF CENTRAL AVENUE; THENCE
2. ALONG SAID PARALLEL LINE, SOUTH 00°03'28" WEST, 208.90 FEET TO THE BEGINNING OF A NON-TANGENT CURVE AT THE NORTHEASTERLY INTERSECTION OF CENTRAL AVENUE AND 73RD STREET (50.00 FEET WIDE, FORMERLY SEVENTY-FOURTH STREET) CONCAVE NORTHERLY, HAVING A RADIUS OF 13.00 FEET, A RADIAL LINE THROUGH THE BEGINNING OF SAID CURVE BEARING SOUTH 57°51'13" WEST; THENCE
3. NORTHERLY ALONG SAID CURVE THROUGH A CENTRAL ANGLE OF 32°12'15" AN ARC DISTANCE OF 7.31 FEET TO A POINT OF TANGENCY ON SAID EASTERLY RIGHT OF WAY LINE OF CENTRAL AVENUE; THENCE
4. ALONG SAID EASTERLY RIGHT OF WAY LINE, PARALLEL WITH AND 50.00 FEET EASTERLY OF SAID CENTERLINE OF CENTRAL AVENUE, NORTH 00°03'28" EAST, 194.97 FEET TO THE BEGINNING OF SAID 27.00-FOOT RADIUS CURVE; THENCE
5. NORTHEASTERLY ALONG SAID 27.00-FOOT RADIUS CURVE THROUGH A CENTRAL ANGLE OF 90°12'04" AN ARC DISTANCE OF 42.51 FEET TO THE **TRUE POINT OF BEGINNING**.

CONTAINING: 548 SQUARE FEET, OR 0.013 ACRES, MORE OR LESS

EXHIBIT “B”: ATTACHED HERETO AND MADE A PART HEREOF.

PROJECT NAME: 73RD STREET AND ALLEYS
EAST OF CENTRAL AVENUE
73RD STREET (1-2RE)
A.M.B. 6024-001
I.M. 099-197
R.D. 241
S.D. 2
LV19000342

PARCEL B, NO. 1-2RE: (EASEMENT FOR PUBLIC ROAD AND HIGHWAY PURPOSES)

THOSE PORTIONS OF LOTS 800 THROUGH 805, INCLUSIVE, IN THE UNINCORPORATED TERRITORY OF THE COUNTY OF LOS ANGELES, STATE OF CALIFORNIA, AS SHOWN ON TRACT NO. 5450, RECORDED IN BOOK 59, PAGES 94 AND 95 OF MAPS, IN THE OFFICE OF THE RECORDER FOR SAID COUNTY, DESCRIBED AS FOLLOWS:

COMMENCING AT THE CENTERLINE INTERSECTION OF 74TH STREET (50.00 FEET WIDE, FORMERLY SEVENTY-FIFTH STREET), AND CENTRAL AVENUE (100.00 FEET WIDE); THENCE ALONG SAID CENTERLINE OF 74TH STREET, SOUTH 89°44'15" WEST, 50.00 FEET TO THE SOUTHERLY PROLONGATION OF THE EASTERLY RIGHT OF WAY LINE OF CENTRAL AVENUE; THENCE ALONG SAID SOUTHERLY PROLONGATION, NORTH 00°03'28" EAST, 25.00 FEET TO THE NORTHERLY RIGHT OF WAY LINE OF 74TH STREET AND THE **TRUE POINT OF BEGINNING**; THENCE THE FOLLOWING NUMBERED COURSES:

1. ALONG SAID EASTERLY RIGHT OF WAY LINE OF CENTRAL AVENUE, NORTH 00°03'28" EAST, 240.11 FEET TO ITS INTERSECTION WITH THE SOUTHERLY RIGHT OF WAY LINE OF 73RD STREET (50.00 FEET WIDE, FORMERLY SEVENTY-FOURTH STREET); THENCE
2. ALONG SAID SOUTHERLY RIGHT OF WAY LINE, NORTH 89°44'26" EAST, 2.00 FEET TO A LINE PARALLEL WITH AND 52.00 FEET EASTERLY OF SAID CENTERLINE OF CENTRAL AVENUE; THENCE
3. ALONG SAID PARALLEL LINE, SOUTH 00°03'28" WEST, 220.17 FEET; THENCE
4. SOUTH 44°50'24" EAST, 21.18 FEET TO A LINE PARALLEL WITH AND 30.00 FEET NORTHERLY OF SAID CENTERLINE OF 74TH STREET; THENCE
5. AT RIGHT ANGLES TO SAID CENTERLINE OF 74TH STREET, SOUTH 00°15'45" WEST, 5.00 FEET TO SAID NORTHERLY RIGHT OF WAY LINE OF 74TH STREET; THENCE
6. ALONG SAID NORTHERLY RIGHT OF WAY LINE, NORTH 89°44'15" WEST, 16.93 FEET TO THE **TRUE POINT OF BEGINNING**.

CONTAINING: 667 SQUARE FEET, OR 0.015 ACRES, MORE OR LESS

EXHIBIT "B": ATTACHED HERETO AND MADE A PART HEREOF.

PREPARED BY ME OR UNDER MY SUPERVISION:




ROBERT WALKER, L.S. 7137

03/14/2022
DATE



EXHIBIT "B"

STREET DEDICATION

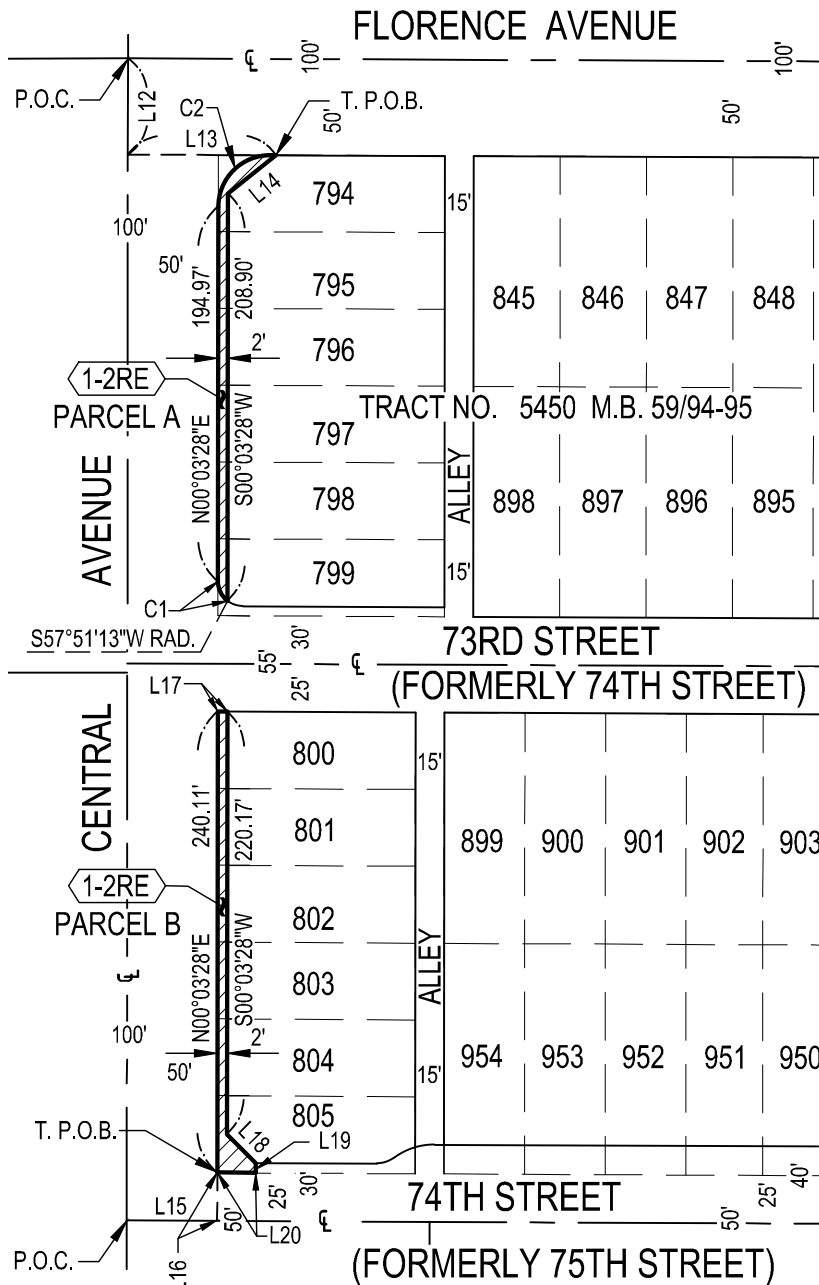

LEGEND




DEDICATION AREA: PARCEL A: 548 S.F. OR 0.013 AC.
PARCEL B: 667 S.F. OR 0.015 AC.

P.O.C. POINT OF COMMENCEMENT

T.P.O.B. TRUE POINT OF BEGINNING

CURVE DATA TABLE			
CURVE #	DELTA	RADIUS	LENGTH
C1	32°12'15"	13.00'	7.31'
C2	90°12'04"	27.00'	42.51'

LINE TABLE		
NO.	BEARING	LENGTH
L12	S00°03'28"W	50.00'
L13	S89°44'28"E	77.10'
L14	S51°30'14"W	32.09'
L15	S89°44'15"W	50.00'
L16	N00°03'28"E	25.00'
L17	S89°44'26"E	2.00'
L18	S44°50'24"E	21.18'
L19	S00°15'45"W	5.00'
L20	N89°44'15"W	16.93'

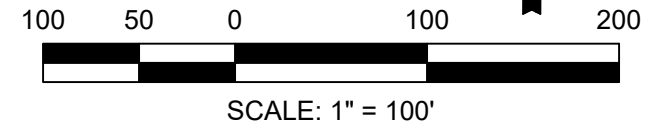

**DAVID EVANS
AND ASSOCIATES INC.**
25152 SPRINGFIELD COURT, SUITE 350
SANTA CLARITA, CA 91355
Phone: 661-284-7400

PROJECT NO:	LAUS0000-0110
SCALE:	1"=100'
DATE:	03/14/2022
SHT NO.:	01 OF 01

PROJECT NAME: 73RD STREET AND ALLEYS
EAST OF CENTRAL AVENUE
73RD STREET (1-3RE)
A.M.B. 6024-001
I.M. 099-197
R.D. 241
S.D. 2
LV19000342

EXHIBIT "C"
LEGAL DESCRIPTION
STREET DEDICATION

PARCEL NO. 1-3RE: (EASEMENT FOR PUBLIC ROAD AND HIGHWAY PURPOSES)

THOSE PORTIONS OF LOTS 805 AND 948 THROUGH 954, INCLUSIVE, IN THE UNINCORPORATED TERRITORY OF THE COUNTY OF LOS ANGELES, STATE OF CALIFORNIA, AS SHOWN ON TRACT NO. 5450, RECORDED IN BOOK 59, PAGES 94 AND 95 OF MAPS, IN THE OFFICE OF THE RECORDER FOR SAID COUNTY, DESCRIBED AS FOLLOWS:

COMMENCING AT THE CENTERLINE INTERSECTION OF CENTRAL AVENUE AND 74TH STREET (FORMERLY SEVENTY-FIFTH STREET, 50.00 FEET WIDE); THENCE ALONG SAID CENTERLINE OF 74TH STREET, SOUTH 89°44'15" EAST, 66.84 FEET; THENCE NORTH 00°15'45" EAST, 25.00 FEET TO THE NORTHERLY RIGHT OF WAY LINE OF 74TH STREET AND THE **TRUE POINT OF BEGINNING**; THENCE THE FOLLOWING NUMBERED COURSES:

1. LEAVING SAID NORTHERLY RIGHT OF WAY LINE, NORTH 00°15'45" EAST, 5.00 FEET TO A LINE PARALLEL WITH AND 30.00 FEET NORTHERLY OF SAID CENTERLINE OF 74TH STREET; THENCE
2. ALONG SAID PARALLEL LINE, SOUTH 89°44'15" EAST, 63.30 FEET TO THE BEGINNING OF A TANGENT CURVE, CONCAVE NORTHERLY, HAVING A RADIUS OF 15.00 FEET; THENCE
3. EASTERLY ALONG SAID CURVE THROUGH A CENTRAL ANGLE OF 36°52'12" AN ARC DISTANCE OF 9.65 FEET TO THE BEGINNING OF REVERSE CURVE, CONCAVE SOUTHERLY, HAVING A RADIUS OF 35.00 FEET, A RADIAL LINE THROUGH THE BEGINNING OF SAID REVERSE CURVE BEARING NORTH 36°36'27" WEST; THENCE
4. EASTERLY ALONG SAID 35.00 FOOT RADIUS CURVE THROUGH A CENTRAL ANGLE OF 36°52'12" AN ARC DISTANCE OF 22.52 FEET TO A POINT OF TANGENCY ON A LINE PARALLEL WITH AND 40.00 FEET NORTHERLY OF SAID CENTERLINE OF 74TH STREET; THENCE
5. ALONG SAID 40.00-FOOT PARALLEL LINE, SOUTH 89°44'15" EAST, 217.43 FEET TO THE BEGINNING OF A TANGENT CURVE, CONCAVE SOUTHERLY HAVING A RADIUS OF 35.00 FEET;
6. EASTERLY ALONG SAID 35.00 FOOT RADIUS CURVE THROUGH A CENTRAL ANGLE OF 36°52'12" AN ARC DISTANCE OF 22.52 FEET TO THE BEGINNING OF REVERSE CURVE, CONCAVE NORTHERLY, HAVING A RADIUS OF 15.00 FEET, A RADIAL LINE THROUGH THE BEGINNING OF SAID REVERSE CURVE BEARING SOUTH 37°07'57" WEST; THENCE
7. EASTERLY ALONG SAID REVERSE CURVE THROUGH A CENTRAL ANGLE OF 36°52'12" AN ARC DISTANCE OF 9.65 FEET TO A POINT OF TANGENCY ON SAID PARALLEL LINE 30.00 FEET NORTHERLY OF THE CENTERLINE OF 74TH STREET; THENCE
8. ALONG SAID 30.00-FOOT PARALLEL LINE, SOUTH 89°44'15" EAST, 8.38 FEET; THENCE
9. SOUTH 00°15'45" WEST, 5.00 FEET TO SAID NORTHERLY RIGHT OF WAY LINE; THENCE
10. ALONG SAID NORTHERLY RIGHT OF WAY LINE, NORTH 89°44'15" WEST, 349.11 FEET TO THE **TRUE POINT OF BEGINNING**.

EXCEPTING THEREFROM THAT PORTION THEREOF LYING WITHIN THAT CERTAIN ALLEY (15.00 FEET WIDE), EASTERLY OF CENTRAL AVENUE BETWEEN 73RD AND 74TH STREETS (FORMERLY SEVENTY-FOURTH AND SEVENTY-FIFTH STREETS, RESPECTIVELY) DESCRIBED AS FOLLOWS:

BEGINNING AT THE SOUTHWEST CORNER OF SAID LOT 954 AT THE INTERSECTION OF THE EASTERLY RIGHT OF WAY LINE OF SAID ALLEY WITH SAID NORTHERLY RIGHT OF WAY LINE OF 74TH STREET; THENCE

PROJECT NAME: 73RD STREET AND ALLEYS
EAST OF CENTRAL AVENUE
73RD STREET (1-3RE)
A.M.B. 6024-001
I.M. 099-197
R.D. 241
S.D. 2
LV19000342

1. ALONG THE WESTERLY PROLONGATION OF SAID NORTHERLY RIGHT OF WAY LINE, NORTH 89°44'15" WEST, 15.00 FEET TO THE SOUTHEAST CORNER OF SAID LOT 805 AT THE INTERSECTION OF THE WESTERLY RIGHT OF WAY LINE OF SAID ALLEY WITH SAID NORTHERLY RIGHT OF WAY LINE OF 74TH STREET; THENCE
2. ALONG SAID WESTERLY RIGHT OF WAY LINE AND THE EASTERLY LINE OF SAID LOT 805, NORTH 00°03'22" EAST, 13.47 FEET TO THE BEGINNING OF A NON-TANGENT CURVE CONCAVE SOUTHEASTERLY, HAVING A RADIUS OF 35.00 FEET, A RADIAL LINE THROUGH THE BEGINNING OF SAID CURVE BEARING NORTH 16°43'09" WEST; THENCE
3. NORTHEASTERLY ALONG SAID CURVE THROUGH A CENTRAL ANGLE OF 16°58'54" AN ARC DISTANCE OF 10.37 FEET TO A POINT OF TANGENCY ON SAID LINE PARALLEL WITH AND 40.00 FEET NORTHERLY OF THE CENTERLINE OF 74TH STREET; THENCE
4. ALONG SAID PARALLEL LINE, SOUTH 89°44'15" EAST, 4.77 FEET TO SAID EASTERLY ALLEY RIGHT OF WAY LINE AND THE WESTERLY LINE OF SAID LOT 954; THENCE
5. ALONG SAID EASTERLY RIGHT OF WAY LINE AND SAID WESTERLY LINE OF LOT 954, SOUTH 00°03'22" WEST, 15.00 FEET TO THE **TRUE POINT OF BEGINNING**.

CONTAINING: 4,044 SQUARE FEET, OR 0.093 ACRES, MORE OR LESS

EXHIBIT "D": ATTACHED HERETO AND MADE A PART HEREOF.

PREPARED BY ME OR UNDER MY SUPERVISION:





ROBERT WALKER, L.S. 7137

02/03/22
DATE



EXHIBIT "D" STREET DEDICATION

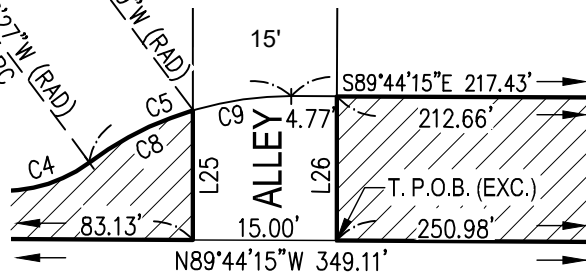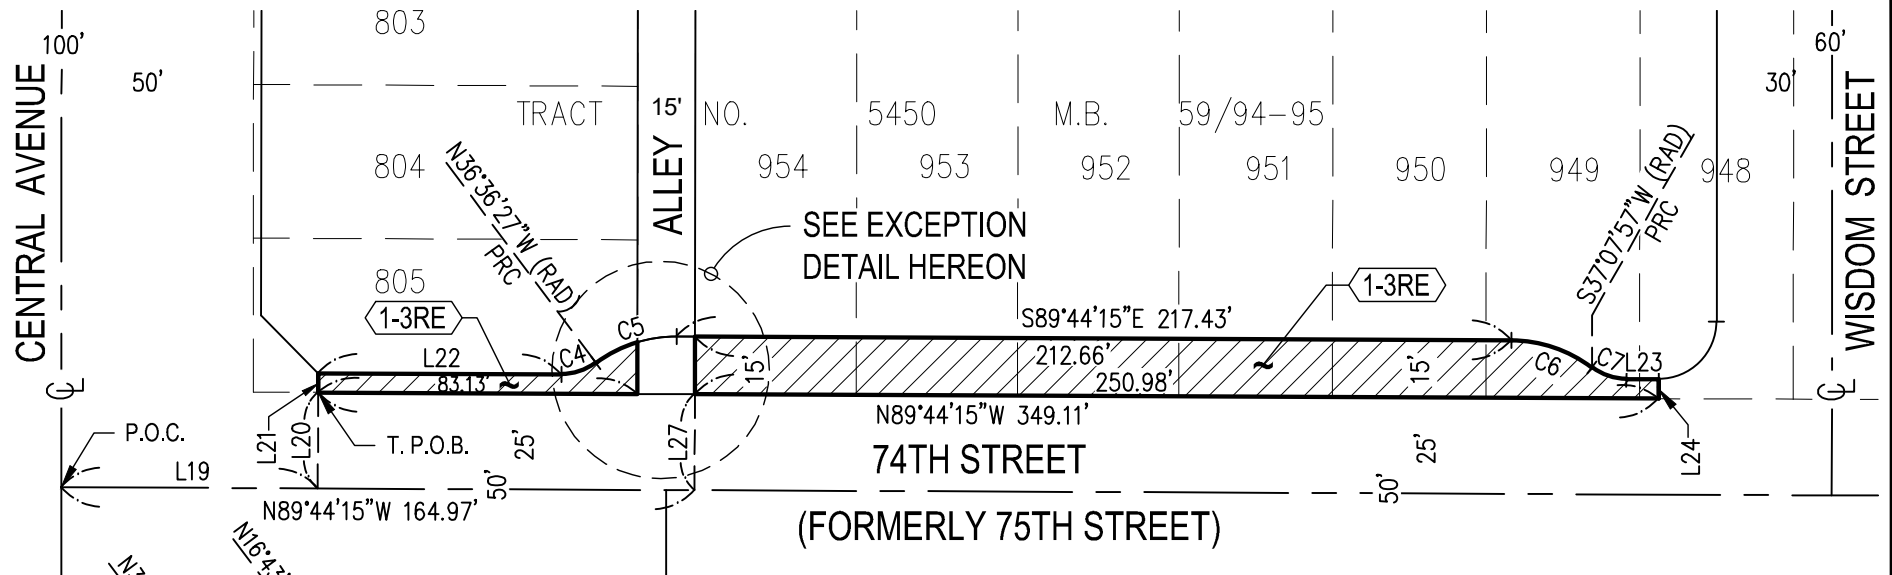

LEGEND



DEDICATION AREA: 4,044 S.F. OR 0.093 AC.

P.O.C. POINT OF COMMENCEMENT

T.P.O.B. TRUE POINT OF BEGINNING



SCALE: 1" = 20'

LINE TABLE		
NO.	BEARING	LENGTH
L19	S89°44'15"E	66.84'
L20	N00°15'45"E	25.00'
L21	N00°15'45"E	5.00'
L22	S89°44'15"E	63.30'
L23	S89°44'15"E	8.38'
L24	S00°15'45"W	5.00'
L25	N00°03'22"E	13.47'
L26	S00°03'22"W	15.00'
L27	N00°15'45"E	25.00'

ARC TABLE			
NO.	DELTA	RADIUS	LENGTH
C4	36°52'12"	15.00'	9.65'
C5	36°52'12"	35.00'	22.52'
C6	36°52'12"	35.00'	22.52'
C7	36°52'12"	15.00'	9.65'
C8	19°53'18"	35.00'	12.15'
C9	16°58'54"	35.00'	10.37'



**DAVID EVANS
AND ASSOCIATES INC.**

25152 SPRINGFIELD COURT, SUITE 350
SANTA CLARITA, CA 91355
Phone: 661-284-7400

PROJECT NO:
LAUS0000-0110
SCALE:
1"=50'
DATE:
02/03/2022
SHT NO.:
01 OF 01

PROJECT NAME: 73RD STREET AND ALLEYS
EAST OF CENTRAL AVENUE
73RD STREET (1-1RE)
A.M.B. 6024-001
I.M. 099-197
R.D. 241
S.D. 2
LV19000342

EXHIBIT "E"
LEGAL DESCRIPTION
STREET DEDICATION

PARCEL NO. 1-1RE: (EASEMENT FOR PUBLIC ROAD AND HIGHWAY PURPOSES)

THOSE PORTIONS OF LOTS 904, 905, 906, 947 AND 948, IN THE UNINCORPORATED TERRITORY OF THE COUNTY OF LOS ANGELES, STATE OF CALIFORNIA, AS SHOWN ON TRACT NO. 5450, RECORDED IN BOOK 59, PAGES 94 AND 95 OF MAPS, IN THE OFFICE OF THE RECORDER FOR SAID COUNTY, DESCRIBED AS FOLLOWS:

COMMENCING AT THE CENTERLINE INTERSECTION OF CENTRAL AVENUE AND 74TH STREET (FORMERLY SEVENTY-FIFTH STREET, 50.00 FEET WIDE); THENCE ALONG SAID CENTERLINE OF 74TH STREET, SOUTH 89°44'15" EAST, 415.95 FEET; THENCE NORTH 00°15'45" EAST, 25.00 FEET TO THE NORTHERLY RIGHT OF WAY LINE OF 74TH STREET AND THE **TRUE POINT OF BEGINNING**; THENCE THE FOLLOWING NUMBERED COURSES:

1. LEAVING SAID NORTHERLY RIGHT OF WAY LINE, NORTH 00°15'45" EAST, 5.00 FEET TO THE BEGINNING OF A NON-TANGENT CURVE, CONCAVE NORTHWESTERLY, HAVING A RADIUS OF 15.00 FEET; THENCE
2. NORTHEASTERLY ALONG SAID CURVE THROUGH A CENTRAL ANGLE OF 90°12'40" AN ARC DISTANCE OF 23.62 FEET TO A LINE PARALLEL WITH AND 60.00 FEET WESTERLY OF THE EASTERLY LINES OF SAID LOTS 906 AND 947 OF TRACT NO. 5450; THENCE
3. ALONG SAID PARALLEL LINE, NORTH 00°03'05" EAST, 113.08 FEET TO THE BEGINNING OF A TANGENT CURVE, CONCAVE WESTERLY HAVING A RADIUS OF 90.00 FEET; THENCE
4. NORTHERLY ALONG SAID 90.00 FOOT RADIUS CURVE THROUGH A CENTRAL ANGLE OF 18°20'19" AN ARC DISTANCE OF 28.81 FEET; THENCE
5. TANGENT TO SAID 90.00 FOOT RADIUS CURVE, NORTH 18°17'15" WEST, 38.43 FEET TO THE BEGINNING OF A TANGENT CURVE, CONCAVE EASTERLY HAVING A RADIUS OF 70.00 FEET; THENCE
6. NORTHERLY ALONG SAID 70.00 FOOT RADIUS CURVE THROUGH A CENTRAL ANGLE OF 35°08'54" AN ARC DISTANCE OF 42.94 FEET; THENCE
7. SOUTH 89°44'26" EAST, 77.23 FEET TO THE NORTHEAST CORNER OF SAID LOT 906; THENCE
8. ALONG SAID EASTERLY LINE OF LOTS 906 AND 947, SOUTH 00°03'05" WEST, 240.14 FEET TO SAID NORTHERLY RIGHT OF WAY LINE OF 74TH STREET; THENCE
9. ALONG SAID NORTHERLY RIGHT OF WAY LINE, NORTH 89°44'15" WEST, 75.07 FEET TO THE **TRUE POINT OF BEGINNING**.

CONTAINING: 15,770 SQUARE FEET, OR 0.362 ACRES, MORE OR LESS

EXHIBIT "F": ATTACHED HERETO AND MADE A PART HEREOF.

PREPARED BY ME OR UNDER MY SUPERVISION:




ROBERT WALKER, L.S. 7137

02/03/22
DATE



EXHIBIT "F" STREET DEDICATION

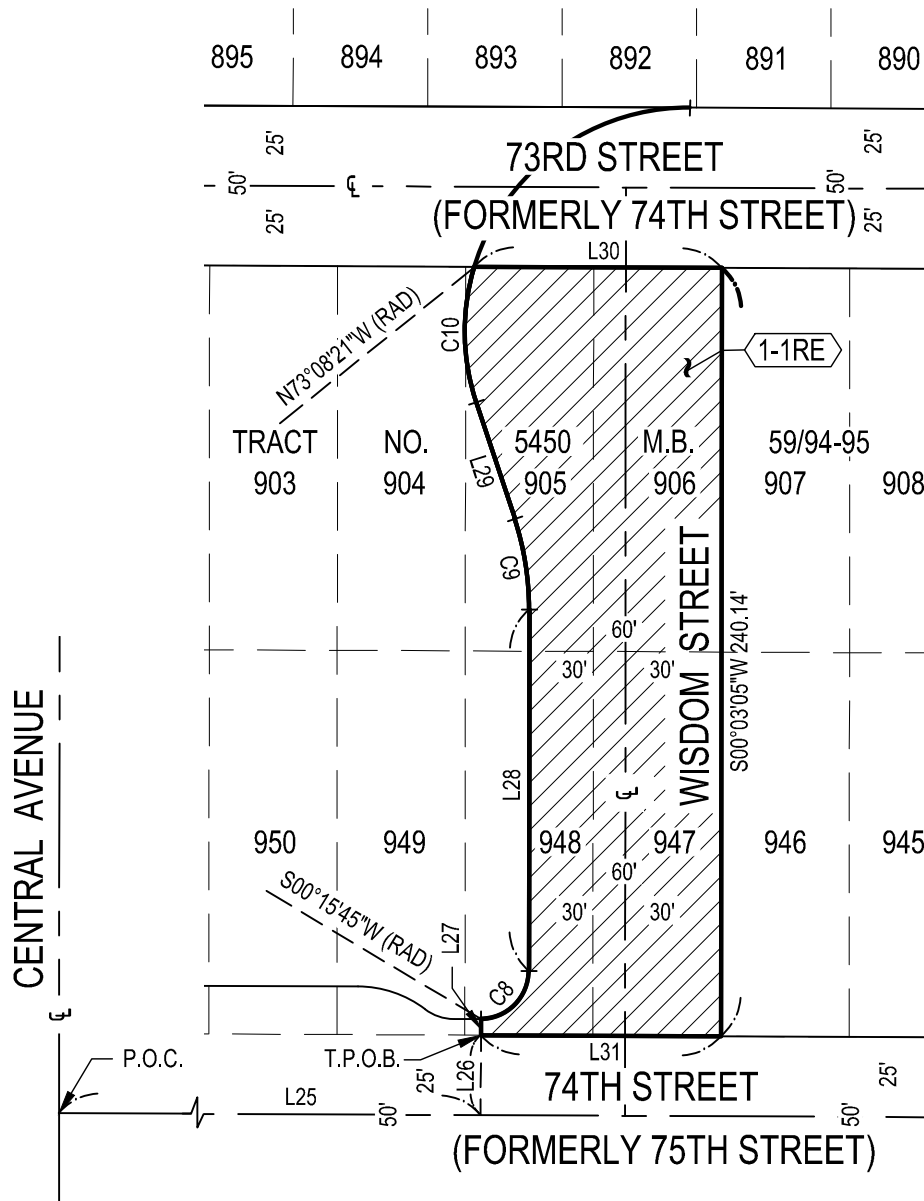

LEGEND



DEDICATION AREA: 15,770 S.F. OR 0.362 AC.

P.O.C. POINT OF COMMENCEMENT

T.P.O.B. TRUE POINT OF BEGINNING

LINE TABLE		
NO.	BEARING	LENGTH
L25	S89°44'15"E	415.95'
L26	N00°15'45"E	25.00'
L27	N00°15'45"E	5.00'
L28	N00°03'05"E	113.08'
L29	N18°17'15"W	38.43'
L30	S89°44'26"E	77.23'
L31	N89°44'15"W	75.07'

ARC TABLE			
NO.	DELTA	RADIUS	LENGTH
C8	90°12'40"	15.00'	23.62'
C9	18°20'19"	90.00'	28.81'
C10	35°08'54"	70.00'	42.94'



SCALE: 1" = 60'



**DAVID EVANS
AND ASSOCIATES INC.**
25152 SPRINGFIELD COURT, SUITE 350
SANTA CLARITA, CA 91355
Phone: 661-284-7400

PROJECT NO:
LAUS0000-0110
SCALE:
1"=60'
DATE:
02/03/2022
SHT NO.:
01 OF 01

EXHIBIT G

NOTICE OF ADOPTION OF RESOLUTION OF INTENTION TO DEDICATE EASEMENTS, REQUIRED FOR THE CONSTRUCTION OF THE SOUTH REGION ELEMENTARY SCHOOL NO. 2 PROJECT, AT WISDOM ELEMENTARY SCHOOL

At the January 17, 2023, meeting of the Board of Education ("Board") of the Los Angeles Unified School District ("Los Angeles Unified"), the following resolution was adopted by at least a two-thirds vote of all its members:

RESOLVED: That the Board, in pursuance of the provisions of Sections 17556 through 17561, inclusive, of the Education Code of the State of California, does hereby declare its intention to irrevocably offer to dedicate easements at Wisdom Elementary School ("Wisdom Elementary") to the County of Los Angeles, a municipal corporation, (hereinafter called Grantee) over all that certain real property situated in the County of Los Angeles, State of California, legally described on Exhibits A, C and E and also shown on Exhibits B, D and F attached hereto.

The proposed dedication of easements to the Grantee will help complete the requirements of the pending street vacation request. The dedication of easements will be in the form of a Roadway Deed for the street and alley easements, as legally described in Exhibits A, C and E and also shown on Exhibits B, D and F attached hereto.

The Grantee shall be responsible for damage caused intentionally or by any negligent act or omission of the respective grantee, its agent or employees while exercising the rights granted respectively herein.

BE IT FURTHER RESOLVED: That a public meeting of this Board be held in the Los Angeles Unified Board Room, 333 South Beaudry Avenue, 1st Floor, Los Angeles, 90017, the regular place of meeting of this Board, at or about 1:00 p.m., on February 07, 2023, for a public hearing upon the question of such dedication.

BE IT FURTHER RESOLVED: That it is the intention of the Board at the time and place fixed for such public hearing or meeting, unless a petition protesting against the proposed dedication, signed by at least ten percent of the qualified electors of Los Angeles Unified, as shown by the affidavit of one of the petitioners, be filed with this Board, to order the dedication and adopt a resolution authorizing the execution and delivery of the dedication of street and alley easements to City of Los Angeles for public use.

Notice of the adoption of this resolution and of the time and place of holding said meeting shall be given by posting copies of this resolution, signed by the members of this Board or a majority thereof, in three public places in this Los Angeles Unified of Los Angeles County, not less than 10 days before the date of said meeting and by publishing a copy of this resolution once not less than five days before the date of said meeting in a newspaper of general circulation published in the Los Angeles Unified of Los Angeles County.

EXHIBIT G

IN WITNESS of the passage of the foregoing Resolution as prescribed by law, we, the Members of said Board, present and voting thereon, have hereunto set our hands the 17th day of January 2023.

[Signature]
[Signature]
[Signature]

[Signature]
Tanya McQuibby Finkel

Jackie Goldberg
Members of the Board of Education of the
City of Los Angeles

ACKNOWLEDGMENT

STATE OF CALIFORNIA

COUNTY OF LOS ANGELES

I, Michael A. McLean, Executive Officer, for the Board of Education of the City of Los Angeles, California, hereby certify the foregoing to be a full, true, and correct copy of Resolution of Intention to Dedicate Easements at Wisdom Elementary.

By: M.A. McLean

Name: Michael A. McLean

Title: Executive Officer of the Board

On January 24, 2023 before me,
Juanita Saavedra, Notary Public (insert name and title of the officer)
personally appeared Michael A. McLean,

who proved to me on the basis of satisfactory evidence to be the person(s) whose name(s) is/are subscribed to the within instrument and acknowledged to me that he/she/they executed the same in his/her/their authorized capacity(ies), and that by his/her/their signature(s) on the instrument the person(s), or the entity upon behalf of which the person(s) acted, executed the instrument.

I certify under PENALTY OF PERJURY under the laws of the State of California that the foregoing paragraph is true and correct.

WITNESS my hand and official seal.

Signature [Signature] (Seal)

